



پلان مبلمان



پلان مبلمان سه بعدی



Isatis Office

Project description: The modeled office is a BIM consultancy company in the construction sector. It is about 80 square meters and is conventionally located in the city of Mashhad.

Contact Information:

LinkedIn: Ali Rahimian

Email Address: Alirahimian21@yahoo.com

Google Scholar: <https://scholar.google.com/citations?user=OqX4L4IAAAJ&hl=en>

Researchgate: <https://www.researchgate.net/profile/Ali-Rahimian-3>

پلان مبلمان

Building Name:

Isatis Office

Date:

29/06/1403

Drawn by:

Ali Rahimian




Checked by:

Checker

The Sheet Number is: A102

Scale _____

1 : 70

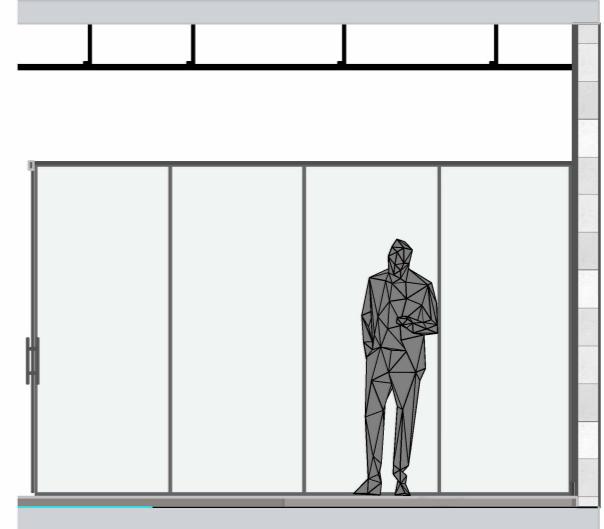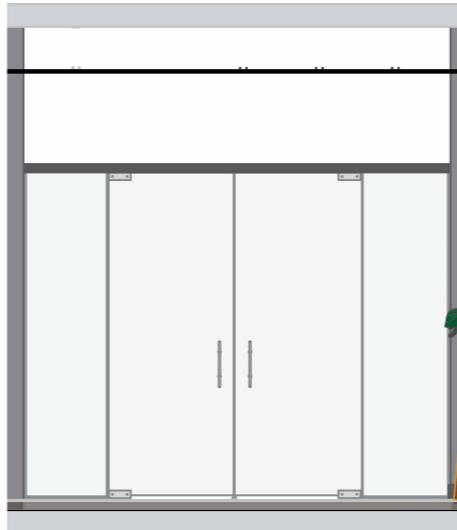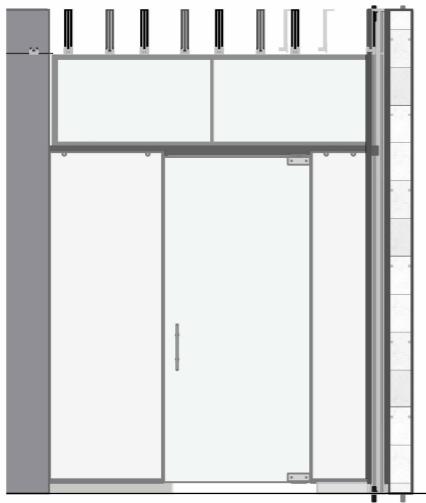


جزیيات دیوار شیشه ای اتاق مدیریت



جزیيات دیوار شیشه ای اتاق پرسنل ۱



جزیيات دیوار شیشه ای اتاق پرسنل ۲

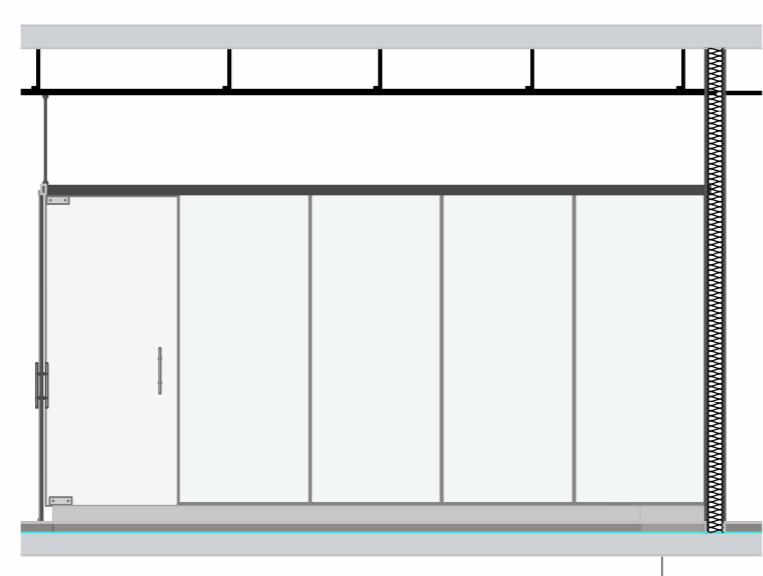

Level 2
3.2 m

Level 1
0 m

جزیيات دیوار شیشه ای اتاق کنفرانس ۱



جزیيات دیوار شیشه ای اتاق کنفرانس ۲



Isatis Office

Project description: The modeled office is a BIM consultancy company in the construction sector. It is about 80 square meters and is conventionally located in the city of Mashhad.

Contact Information:

LinkedIn: Ali Rahimian

Email Address: Alirahimian21@yahoo.com

Google Scholar: <https://scholar.google.com/citations?user=OqX4L4IAAAJ&hl=en>

Researchgate: <https://www.researchgate.net/profile/Ali-Rahimian-3>

پلان دیوارهای شیشه ای

Building Name:
Isatis Office


Date:
29/06/1403

Drawn by:
Author


Checked by:
Checker

The Sheet Number is: A104

Scale
1 : 50

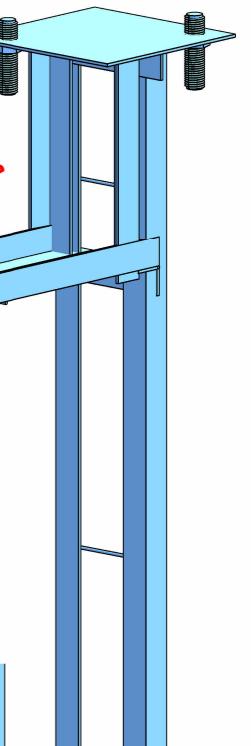

جزییات اتصالات سقف

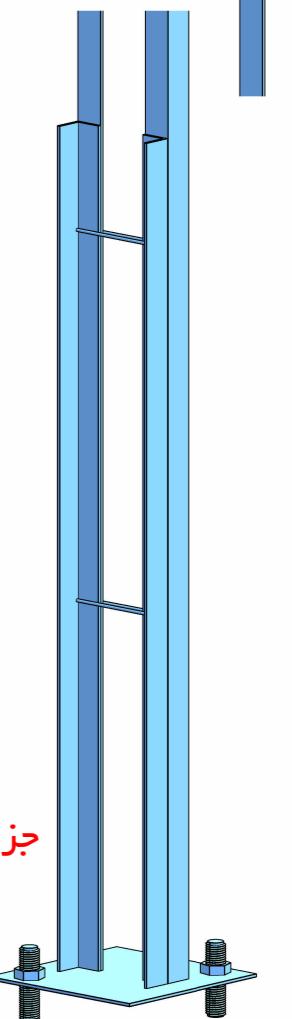

جزییات اتصالات کف

پلان وال پست



جزییات وال پست ۱



پلان جزییات وال پست ها

Isatis Office

Project description: The modeled office is a BIM consultancy company in the construction sector. It is about 80 square meters and is conventionally located in the city of Mashhad.

Contact Information:

LinkedIn: Ali Rahimian

Email Address: Alirahimian21@yahoo.com


Google Scholar: <https://scholar.google.com/citations?user=OqX4L4IAAAJ&hl=en>

Researchgate: <https://www.researchgate.net/profile/Ali-Rahimian-3>


Building Name:
Date:
Drawn by:
Checked by:

Isatis Office
29/06/1403
Author
Checker


The Sheet Number is: A105

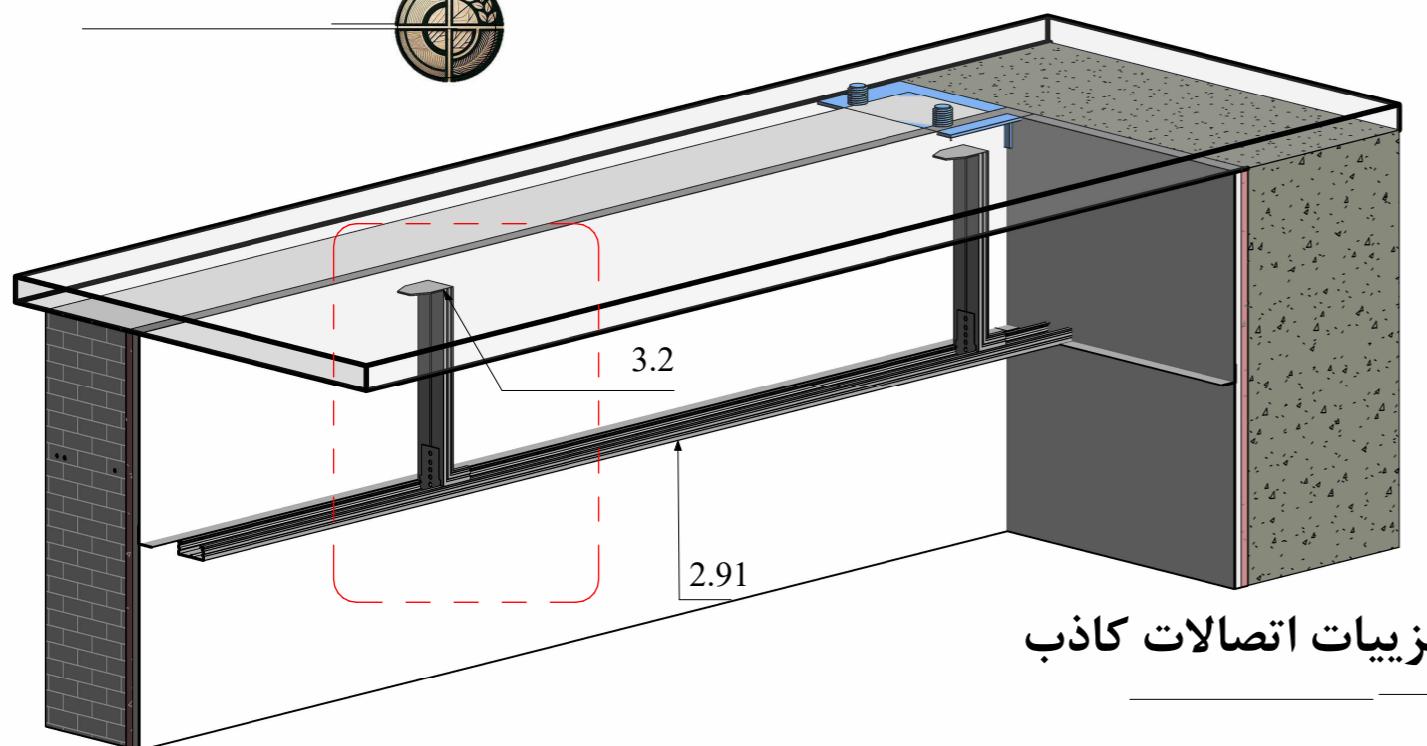

جزییات اتصالات کاذب

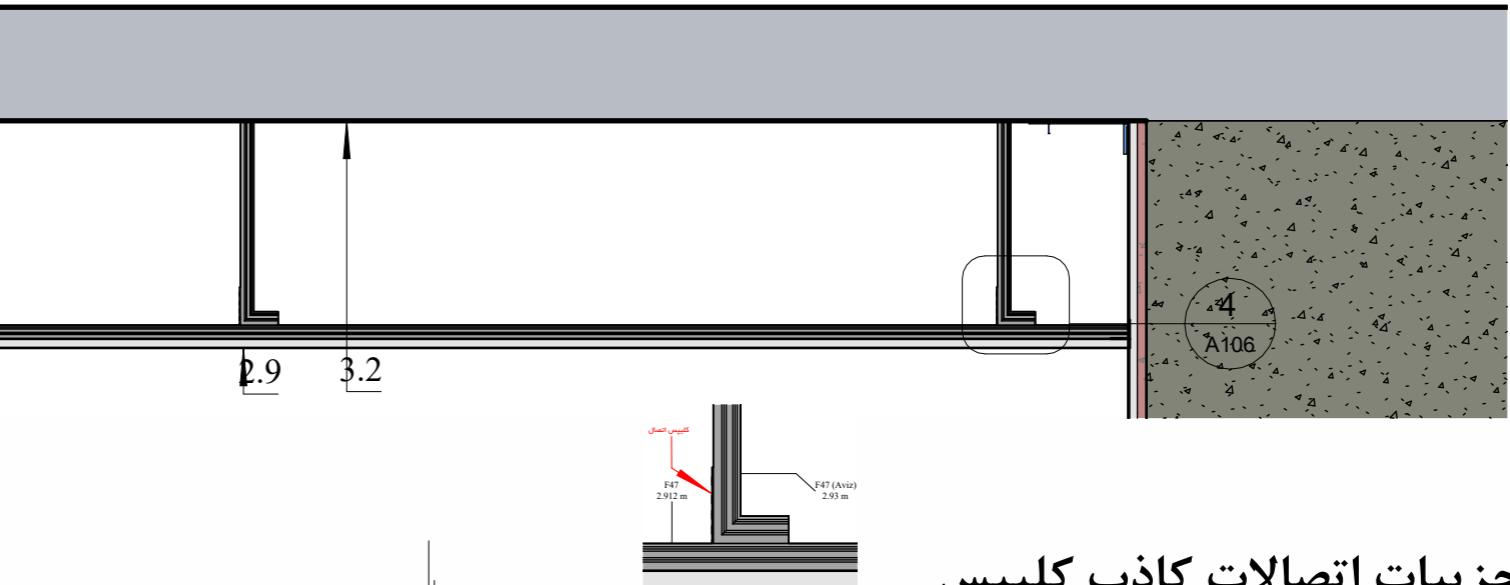

جزییات اتصالات کاذب گلیپس

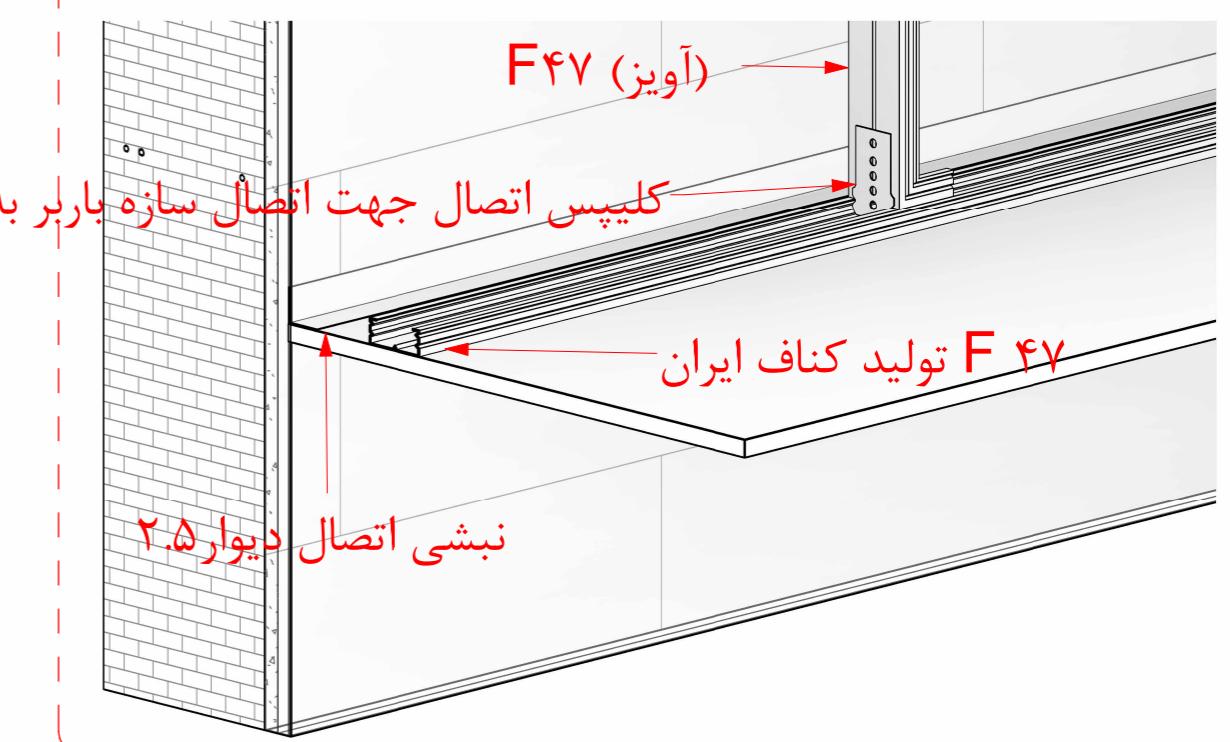

Isatis Office

Project description: The modeled office is a BIM consultancy company in the construction sector. It is about 80 square meters and is conventionally located in the city of Mashhad.

Contact Information:

LinkedIn: Ali Rahimian
Email Address: Alirahimian21@yahoo.com
Google Scholar: <https://scholar.google.com/citations?user=OqX4L4IAAAJ&hl=en>


Researchgate: <https://www.researchgate.net/profile/Ali-Rahimian-3>

سقف کاذب و جزییات

Building Name:	Isatis Office
Date:	29/06/1403
Drawn by:	Author
Checked by:	Checker

The Sheet Number is: A106

Scale As indicated

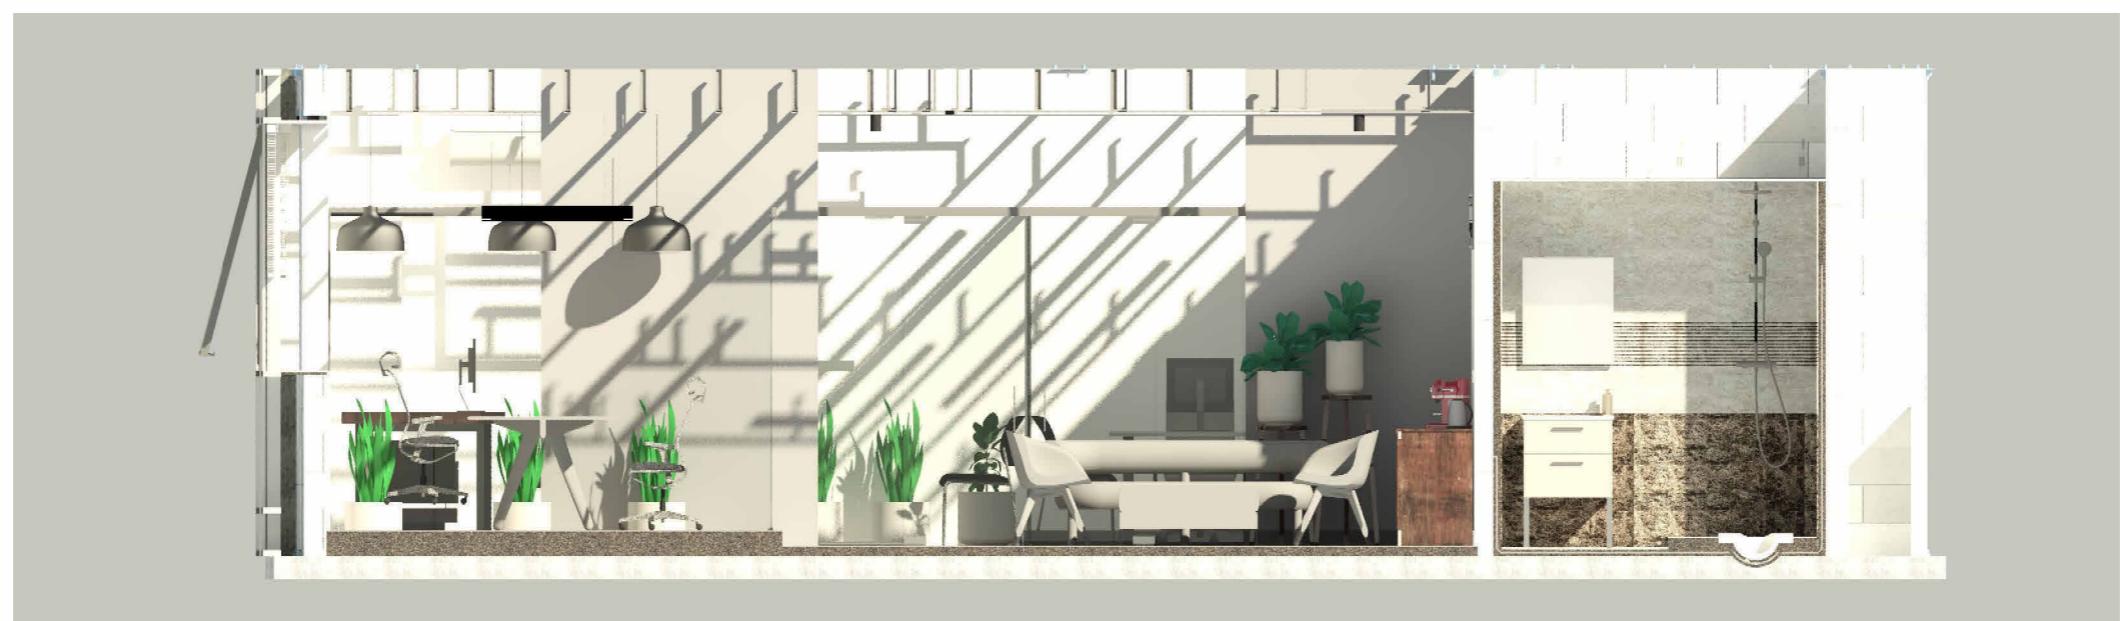

B-B برش



B-B رندر



B-B

Isatis Office

Project description: The modeled office is a BIM consultancy company in the construction sector. It is about 80 square meters and is conventionally located in the city of Mashhad.

Contact Information:

LinkedIn: Ali Rahimian

Email Address: Alirahimian21@yahoo.com

Google Scholar: <https://scholar.google.com/citations?user=OqX4L4IAAAJ&hl=en>


Researchgate: <https://www.researchgate.net/profile/Ali-Rahimian-3>

Building Name:
Date:
Drawn by:
Checked by:


Isatis Office
29/06/1403
Author
Checker

The Sheet Number is: A109


Scale _____ As indicated

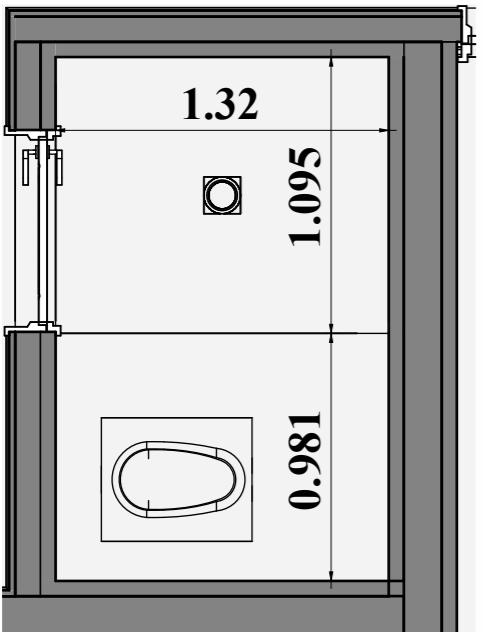


بزرگنمایی سرویس بهداشتی

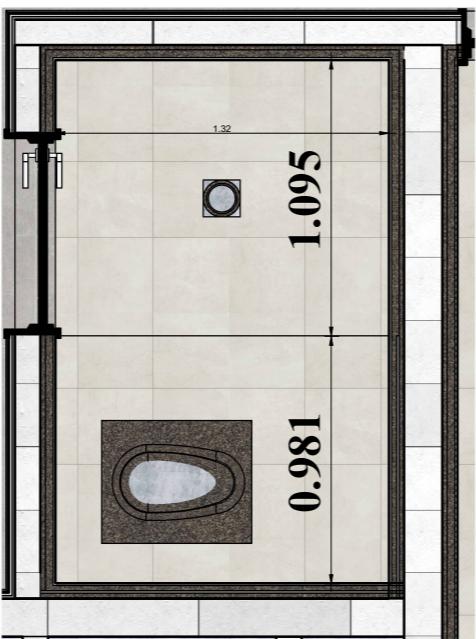

بزرگنمایی سرویس بهداشتی - متریال

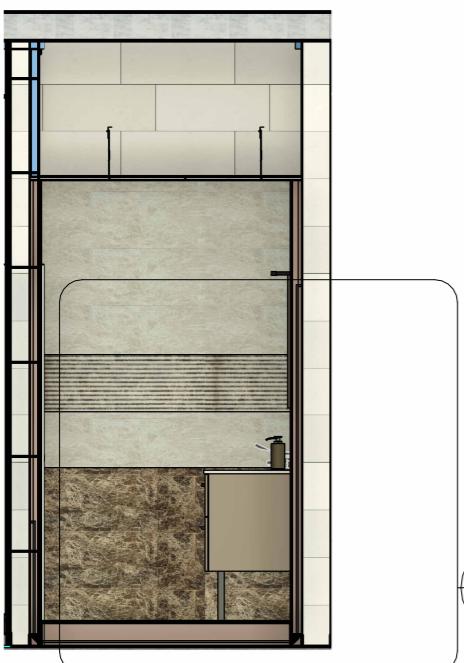

جزیيات سرویس بهداشتی

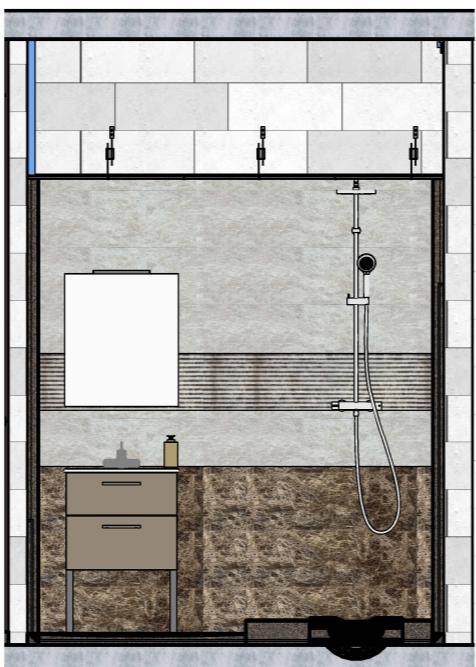

جزیيات متریال های سرویس



سرویس سه بعدی

Isatis Office

Project description: The modeled office is a BIM consultancy company in the construction sector. It is about 80 square meters and is conventionally located in the city of Mashhad.

Contact Information:

LinkedIn: Ali Rahimian

Email Address: Alirahimian21@yahoo.com

Google Scholar: <https://scholar.google.com/citations?user=OqX4L4IAAAJ&hl=en>

Researchgate: <https://www.researchgate.net/profile/Ali-Rahimian-3>

پلان سرویس بهداشتی

Building Name:

Isatis Office

Date:

29/06/1403

Drawn by:


Author

Checked by:


Checker

The Sheet Number is: A110

Scale

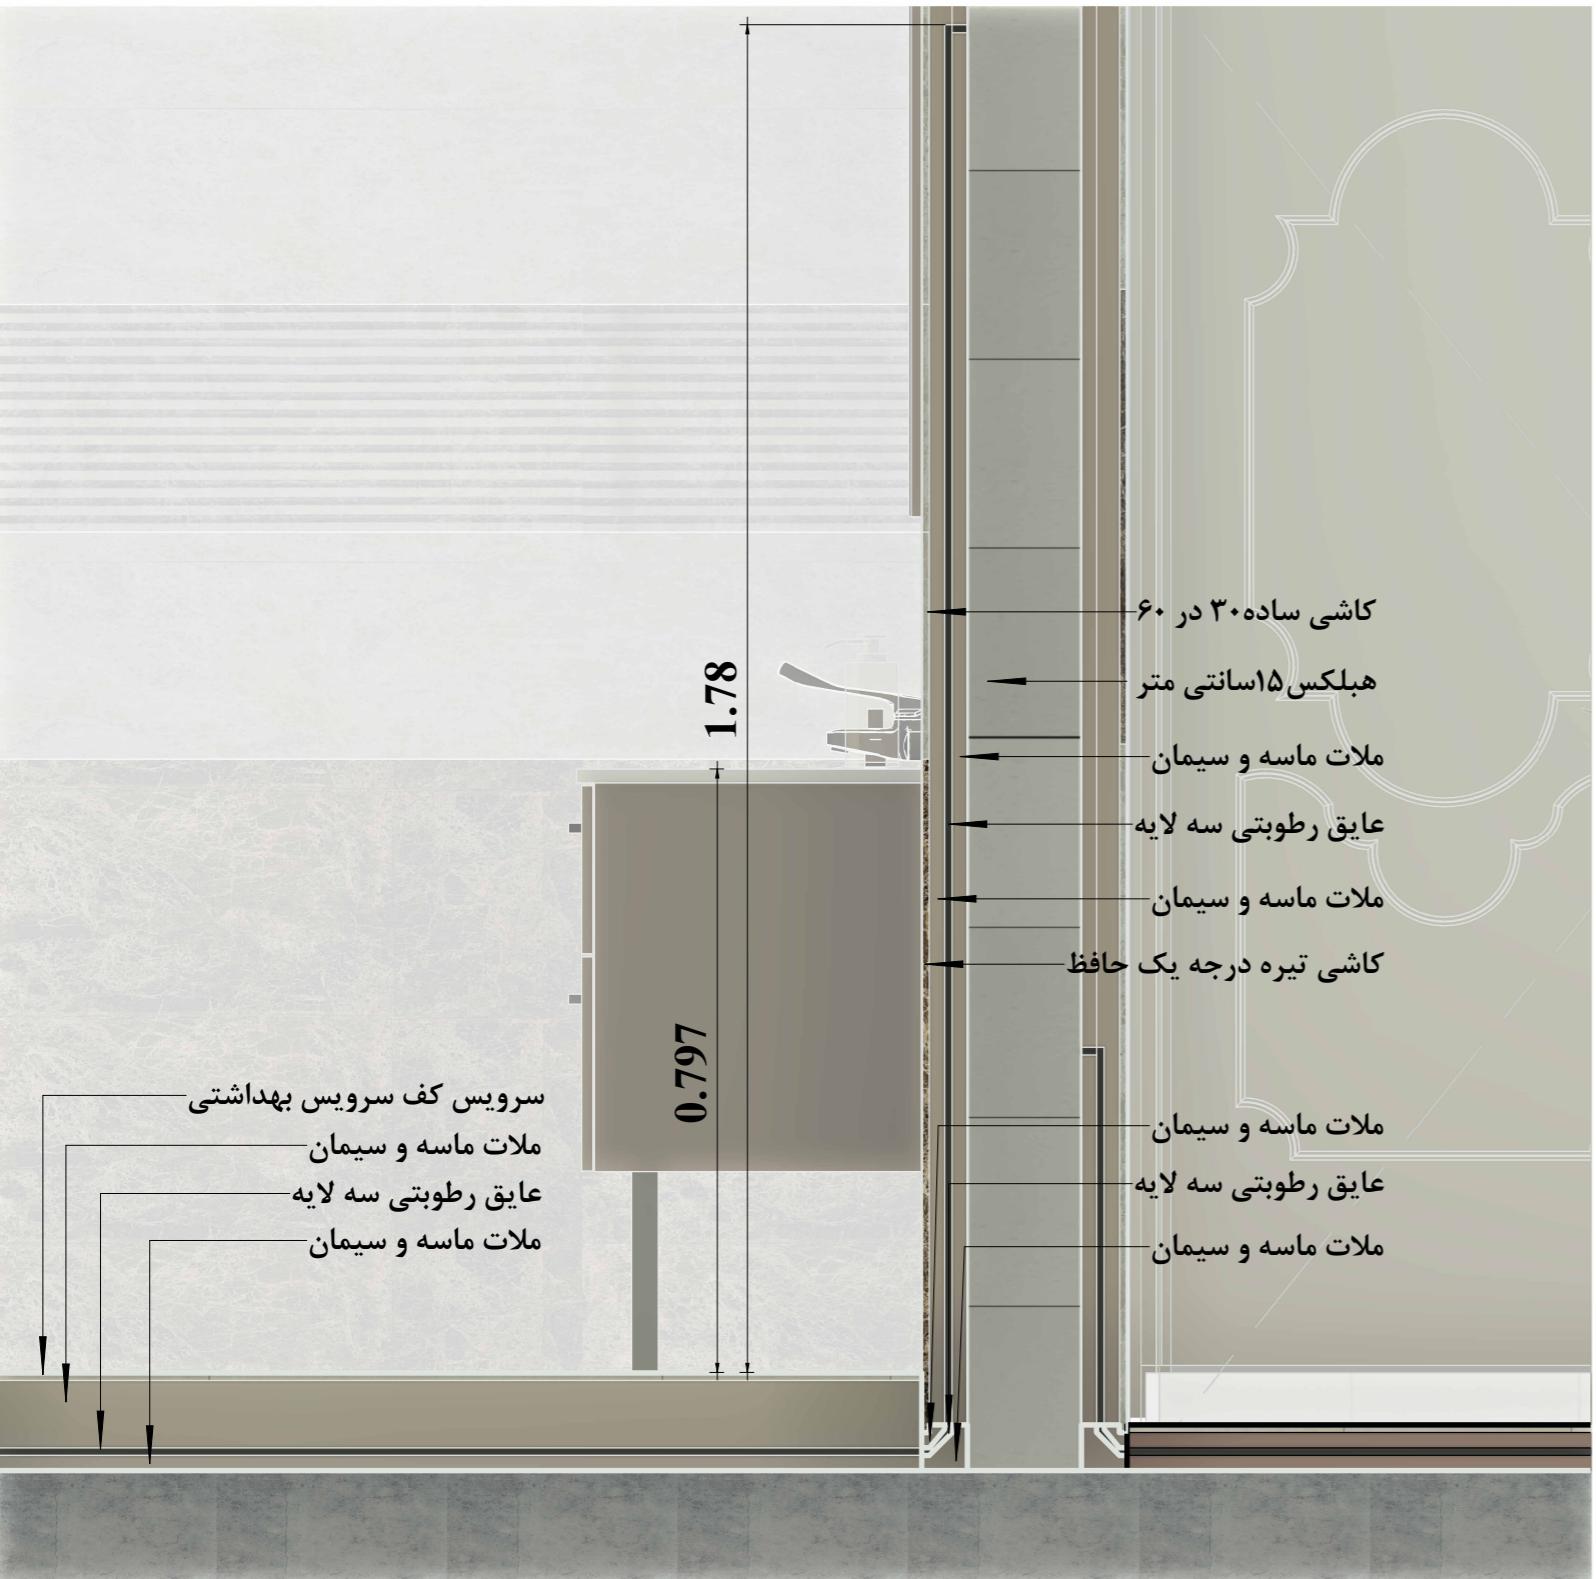

بزرگنمایی اجرایی سرویس - دوش حمام

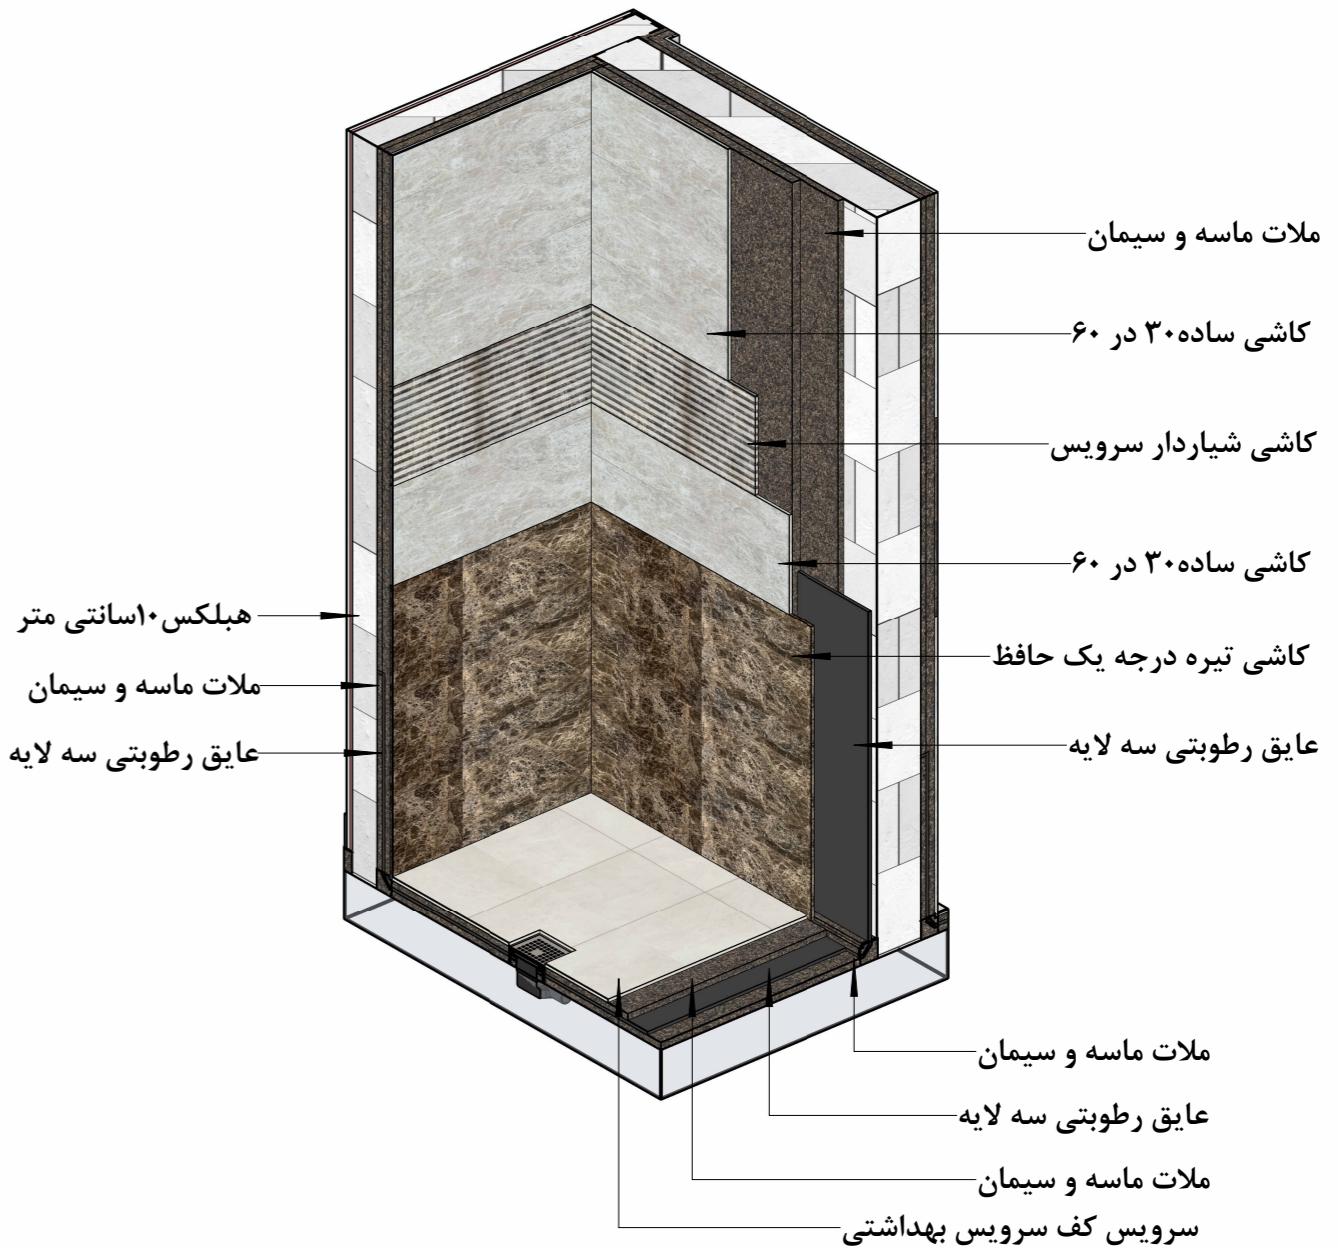

دید جزئیات سه بعدی سرویس

Isatis Office

Project description: The modeled office is a BIM consultancy company in the construction sector. It is about 80 square meters and is conventionally located in the city of Mashhad.

Contact Information:

LinkedIn: Ali Rahimian

Email Address: Alirahimian21@yahoo.com

Google Scholar: <https://scholar.google.com/citations?user=OqX4L4IAAAJ&hl=en>

Researchgate: <https://www.researchgate.net/profile/Ali-Rahimian-3>

جزئیات سرویس بهداشتی

Building Name:

Isatis Office

Date:

29/06/1403

Drawn by:

Author



Checked by:

Checker


The Sheet Number is: A111

Scale _____

جزیات اتصال بالای پنجره

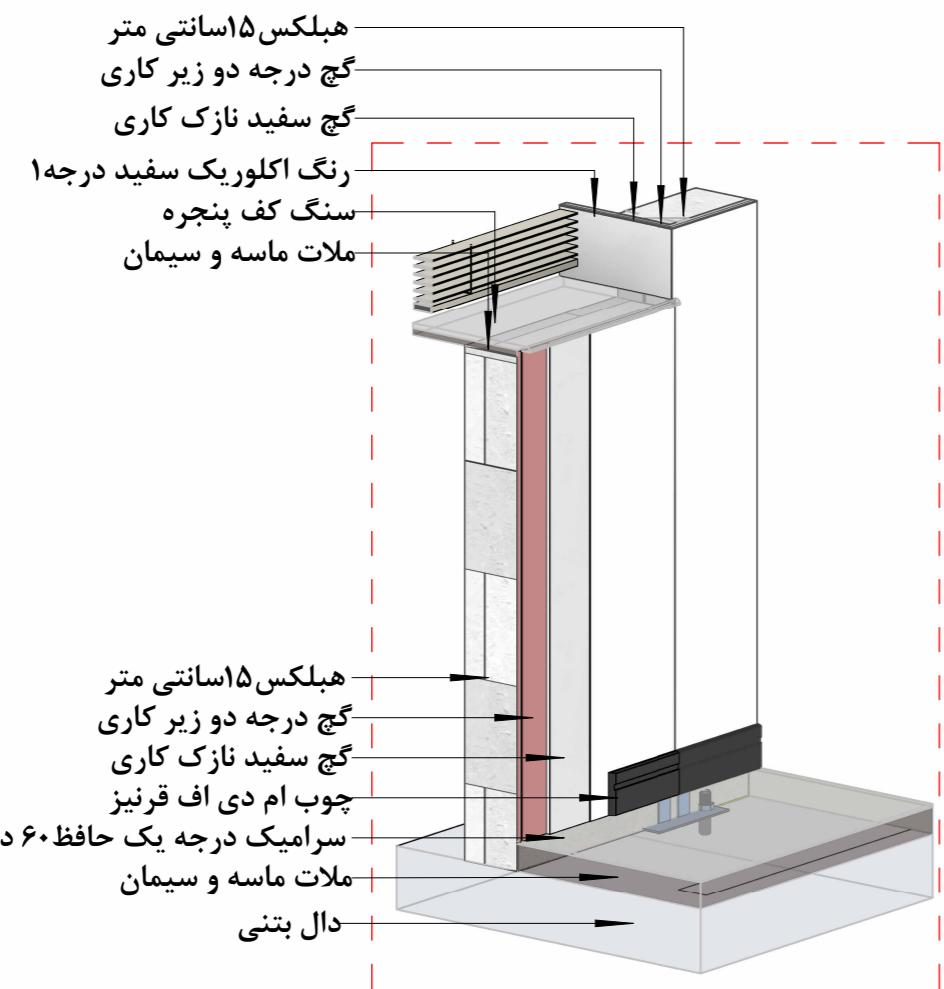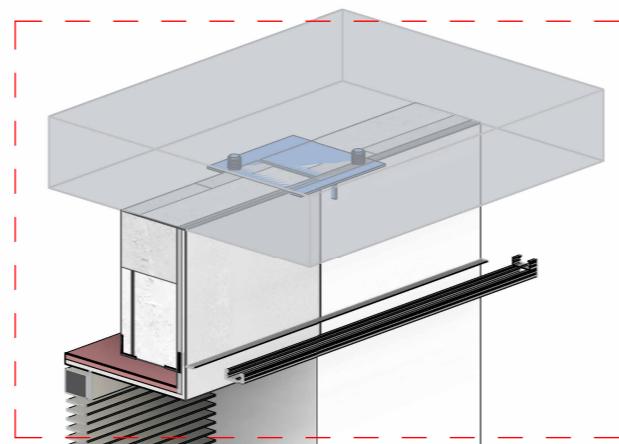

جزیات پایین پنجره

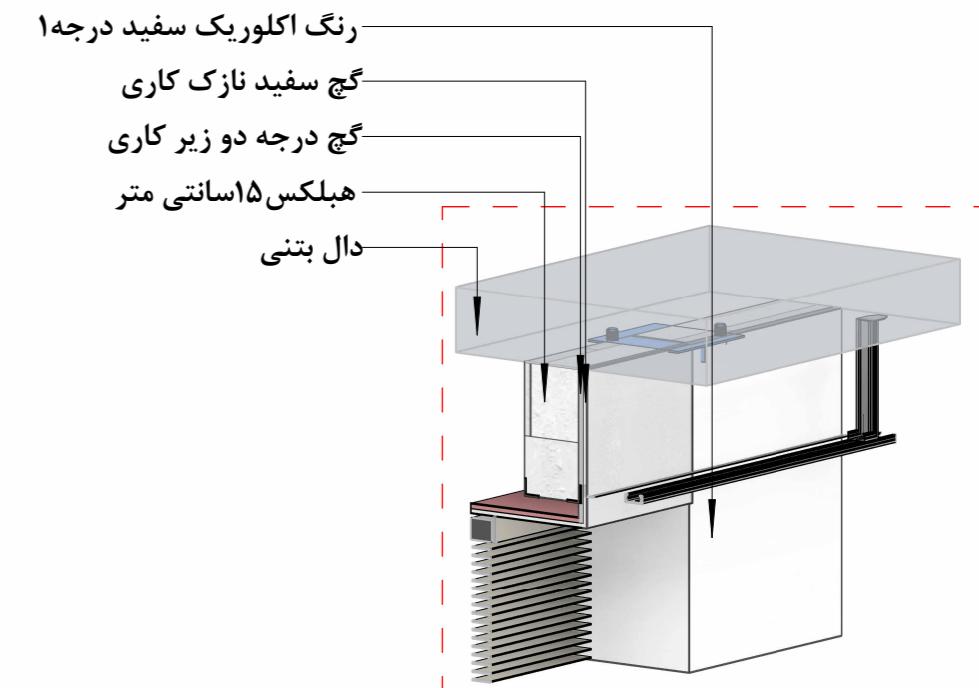

جزیات سه بعدی اتصالات پنجره



Isatis Office

Project description: The modeled office is a BIM consultancy company in the construction sector. It is about 80 square meters and is conventionally located in the city of Mashhad.

Contact Information:

LinkedIn: Ali Rahimian
Email Address: Alirahimian21@yahoo.com
Google Scholar: <https://scholar.google.com/citations?user=OqX4L4IAAAJ&hl=en>
Researchgate: <https://www.researchgate.net/profile/Ali-Rahimian-3>

جزیات اتصالات دیوار پنجره

Building Name:	Isatis Office
Date:	29/06/1403
Drawn by:	Author
Checked by:	Checker

The Sheet Number is: A112
Scale _____

هبلکس ۱۵ اسانسی متر
گچ درجه دو زیر کاری
گچ سفید نازک کاری

شیشه لیمویی رنگ
سنگ کف پنجره
ملات ماسه و سیمان

هبلکس ۱۵ اسانسی متر
گچ درجه دو زیر کاری
گچ سفید نازک کاری
رنگ اکلوریک سفید درجه ۱
چوب ام دی اف قرنیز

2.83

گچ برگ کناف
آلومینیوم سفید
ورق فولادی گالوانیزه

دال بتونی

سرامیک درجه یک حافظ ۶۰ در ۱۲۰

ملات ماسه و سیمان

جزییات دیوار پنجره



جزییات سه بعدی پنجره

Isatis Office

Project description: The modeled office is a BIM consultancy company in the construction sector. It is about 80 square meters and is conventionally located in the city of Mashhad.

Contact Information:

LinkedIn: Ali Rahimian

Email Address: Alirahimian21@yahoo.com

Google Scholar: <https://scholar.google.com/citations?user=OqX4L4IAAAJ&hl=en>

Researchgate: <https://www.researchgate.net/profile/Ali-Rahimian-3>

جزییات دیوار پنجره

Building Name:

Isatis Office

Date:

29/06/1403

Drawn by:

Ali Rahimian

Checked by:

To Be Checked

The Sheet Number is: A113

Scale _____